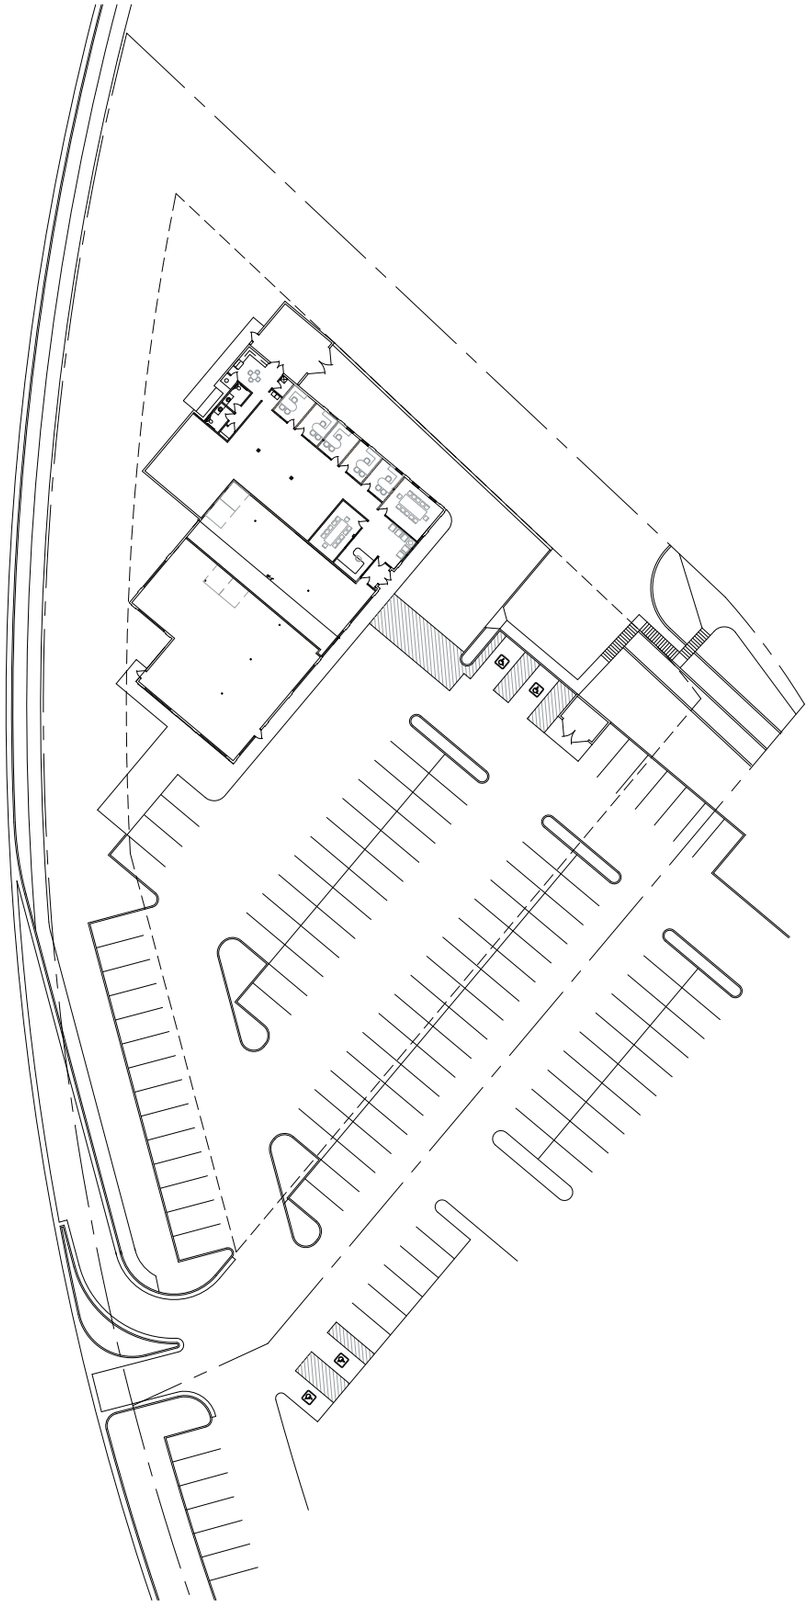

AS-IS SITE PLAN

SCALE: 1"= 40'-0"

NORTH

ELEVATIONAL AREAS:
STONE: 184 SF = 16%
CEMENT BOARD: 513 SF = 45%
METAL/ GLASS: 454 SF = 39%

EAST ELEVATION

SCALE: 1/8" = 1'-0"

ELEVATIONAL AREAS:
STONE: 200 SF = 20%
CEMENT BOARD: 675 SF = 66%
METAL/ GLASS: 144 SF = 14%

WEST ELEVATION

SCALE: 1/8" = 1'-0"

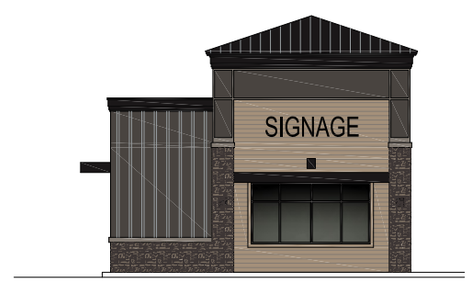

ELEVATIONAL AREAS:
STONE: 83 SF = 13%
CEMENT BOARD: 387 SF = 59%
METAL/ GLASS: 182 SF = 28%

SOUTH ELEVATION

SCALE: 1/8" = 1'-0"

ELEVATIONAL AREAS:
STONE: 158 SF = 26%
CEMENT BOARD: 355 SF = 59%
METAL/ GLASS: 88 SF = 15%

NORTH ELEVATION

SCALE: 1/8" = 1'-0"

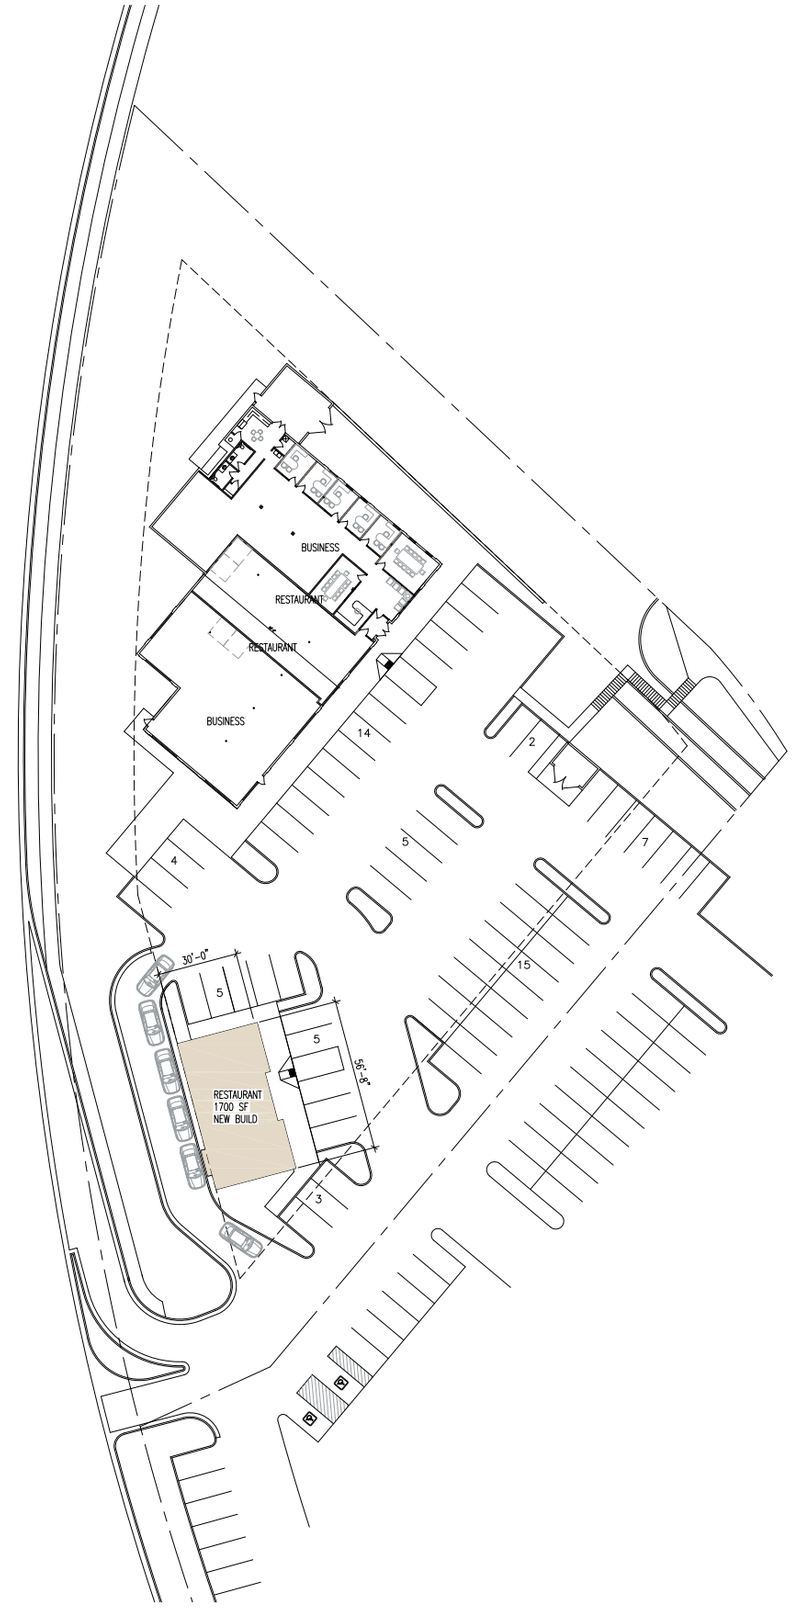

PROPOSED SITE PLAN

SCALE: 1"= 30'-0"

NORTH